


Thai BIM Footing synthetic | S001 | Footing plan

MODEL DETAIL | 1:50 | Dimensions mm / levels m | local Member view / actual cage


USER ไทย: ตรวจระดับฐานราก

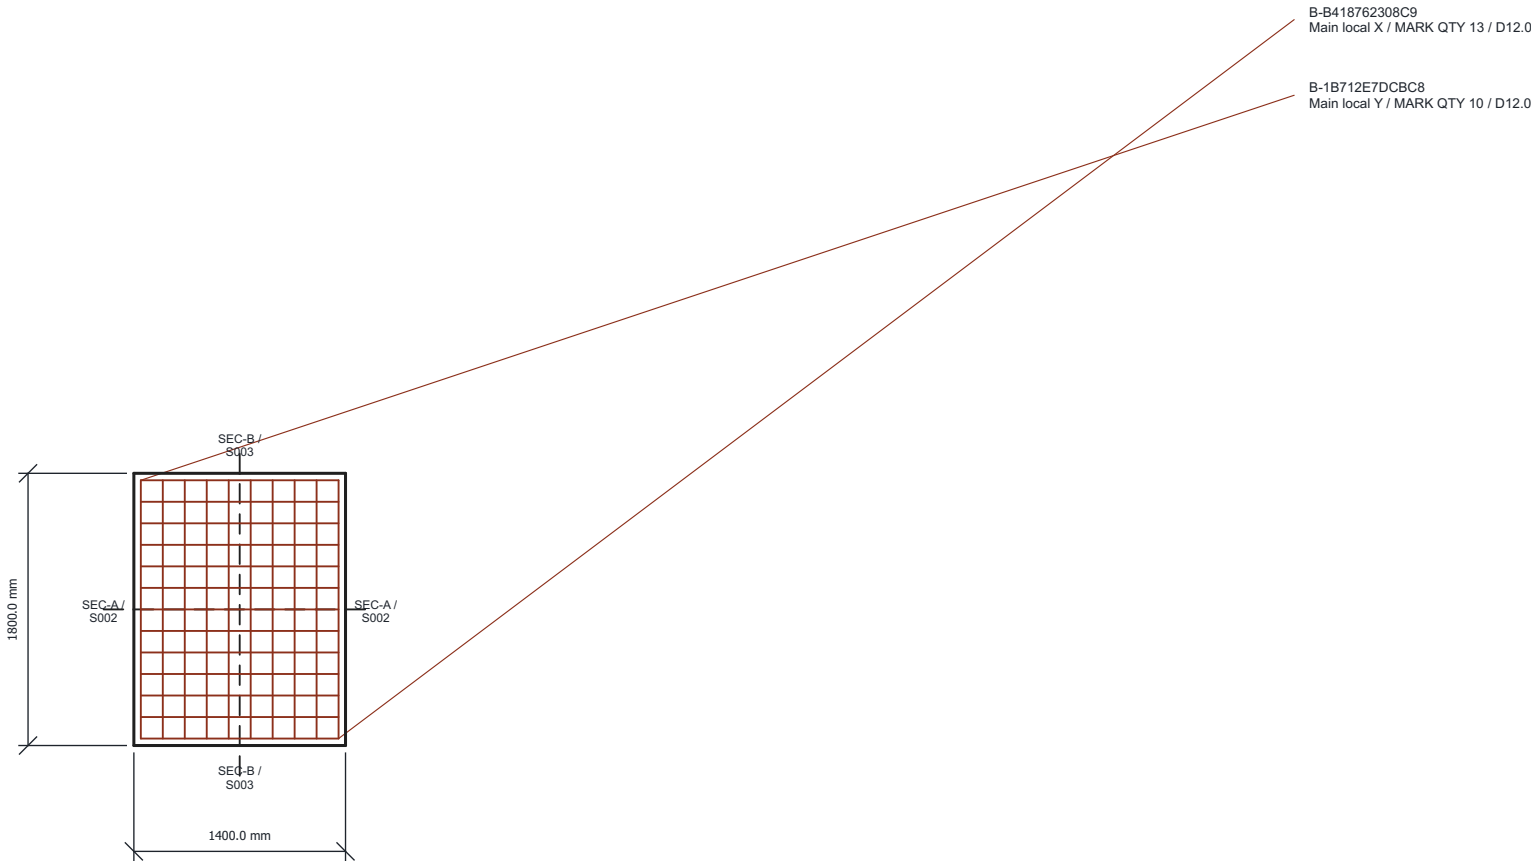

Footing mesh extents 1400 x 1800 x 500 mm | Actual concrete section; heavy = cut, grey = projected context; overall dimensions are local mesh extents. Red = complete actual cage projection (coincident paths overlaid).

Actual cage projected in red; leaders identify representative roles. All marks, counts and cut lengths in details / BBS.


Scale check: 1 m = 20 mm; print at 100%

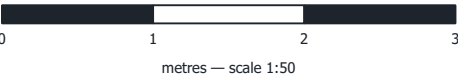

PROJECT: Thai BIM Footing synthetic	DATE: 2026-10-04
SHEET: S001	REV: 01
SCALE: 1:50 @ A3	AUTHOR:
STATUS: MODEL DETAIL / REVIEW	MODEL: Footing

Thai BIM Footing synthetic | S002 | Section A-A / local X


MODEL DETAIL | 1:50 | Dimensions mm / levels m | local Member view / actual cage

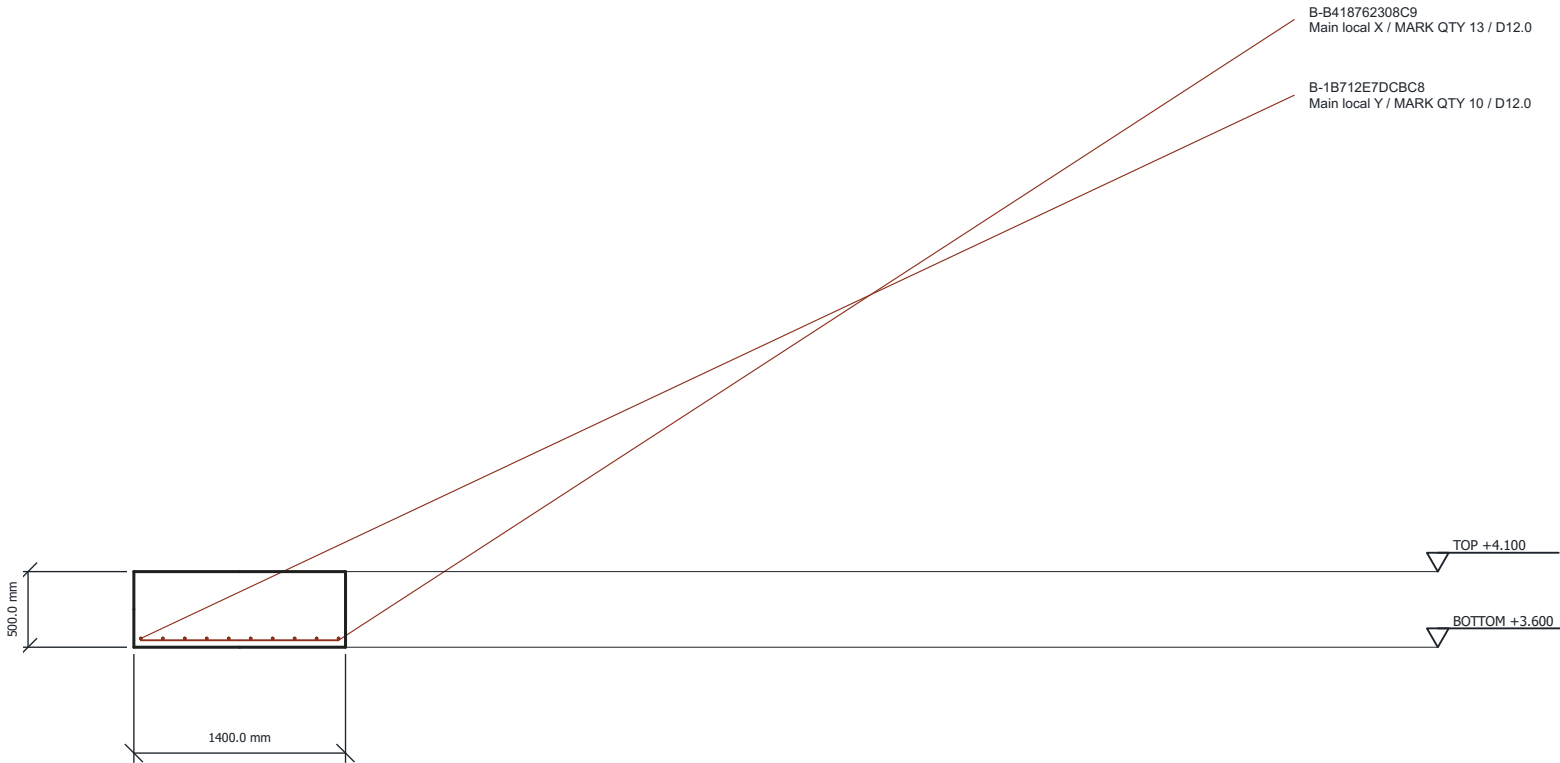

Footing mesh extents 1400 x 1800 x 500 mm | Actual concrete section; heavy = cut, grey = projected context; overall dimensions are local mesh extents. Red = complete actual cage projection (coincident paths overlaid).

Actual cage projected in red; leaders identify representative roles. All marks, counts and cut lengths in details / BBS.


Scale check: 1 m = 20 mm; print at 100%

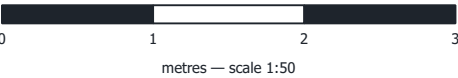

PROJECT: Thai BIM Footing synthetic	DATE: 2026-10-04
SHEET: S002	REV: 01
SCALE: 1:50 @ A3	AUTHOR:
STATUS: MODEL DETAIL / REVIEW	MODEL: Footing

Thai BIM Footing synthetic | S003 | Section B-B / local Y


MODEL DETAIL | 1:50 | Dimensions mm / levels m | local Member view / actual cage

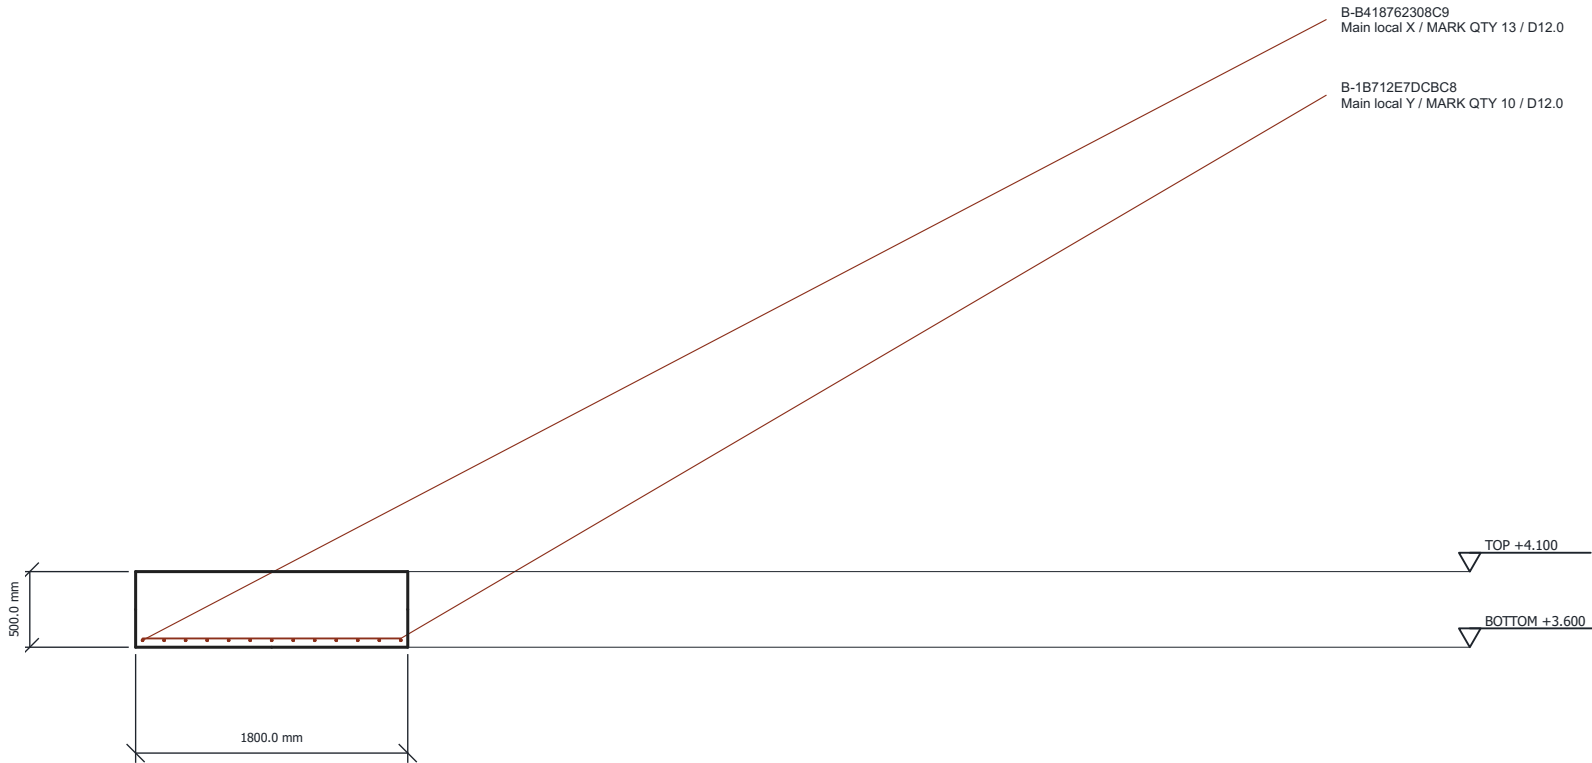

Footing mesh extents 1400 x 1800 x 500 mm | Actual concrete section; heavy = cut, grey = projected context; overall dimensions are local mesh extents. Red = complete actual cage projection (coincident paths overlaid).

Actual cage projected in red; leaders identify representative roles. All marks, counts and cut lengths in details / BBS.

Scale check: 1 m = 20 mm; print at 100%

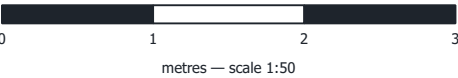

PROJECT: Thai BIM Footing synthetic	DATE: 2026-10-04
SHEET: S003	REV: 01
SCALE: 1:50 @ A3	AUTHOR:
STATUS: MODEL DETAIL / REVIEW	MODEL: Footing


Thai BIM Footing synthetic | S004 | B-1B712E7DCBC8 / Shape plane

MODEL DETAIL | 1:50 | Dimensions mm / levels m | local Member view / actual cage



BAR MARK B-1B712E7DCBC8 | QTY 10 | Diameter 12 mm
ROLE: Main local Y
Cut length 1708.000 mm | Inside bend radius 24 mm
Straight tangent lengths mm: 1708.00
Bend angles deg:
Steel: TIS 24-2559 / DB DB12 SD40
BBS basis: Analytic tangent straights + centreline radius × bend angle

Scale check: 1 m = 20 mm; print at 100%

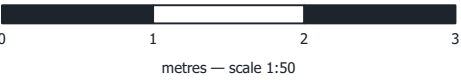

PROJECT: Thai BIM Footing synthetic	DATE: 2026-10-04
SHEET: S004	REV: 01
SCALE: 1:50 @ A3	AUTHOR:
STATUS: MODEL DETAIL / REVIEW	MODEL: Footing


Thai BIM Footing synthetic | S005 | B-B418762308C9 / Shape plane

MODEL DETAIL | 1:50 | Dimensions mm / levels m | local Member view / actual cage



BAR MARK B-B418762308C9 | QTY 13 | Diameter 12 mm
ROLE: Main local X
Cut length 1308.000 mm | Inside bend radius 24 mm
Straight tangent lengths mm: 1308.00
Bend angles deg:
Steel: TIS 24-2559 / DB DB12 SD40
BBS basis: Analytic tangent straights + centreline radius × bend angle

Scale check: 1 m = 20 mm; print at 100%

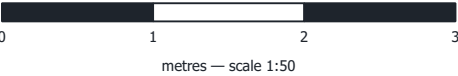

PROJECT: Thai BIM Footing synthetic	DATE: 2026-10-04
SHEET: S005	REV: 01
SCALE: 1:50 @ A3	AUTHOR:
STATUS: MODEL DETAIL / REVIEW	MODEL: Footing

Thai BIM Footing synthetic | BBS01 | Bar bending schedule

BBS SCHEDULE | Table NTS | Actual-cage marks and analytic cut lengths

BAR MARK	ROLE / STEEL	D mm	QTY	CUT m	TOTAL m	MASS kg
B-1B712E7DCBC8	Main local Y TIS 24-2559 / DB DB12 SD40	12	10	1.708	17.080	15.164
B-B418762308C9	Main local X TIS 24-2559 / DB DB12 SD40	12	13	1.308	17.004	15.096

Counts and analytic cut lengths match actual-cage BBS Bar Marks; no procurement waste / laps inferred.

PROJECT: Thai BIM Footing synthetic	DATE: 2026-10-04
SHEET: BBS01	REV: 01
SCALE: NTS / table	AUTHOR:
STATUS: MODEL DETAIL / REVIEW	MODEL: Footing